


Inverter	N. Moduli	P. Nominale del Generatore(kW)	P. Inverter (kW)	P. Nominale in uscita dell'inverter (kW)
A	108	49,68	50	49,68
B	108	49,68	50	49,68
	216	99,36	100	99,36

DETTAGLIO IMPIANTO FOTOVOLTAICO
Potenza per singolo Inverter

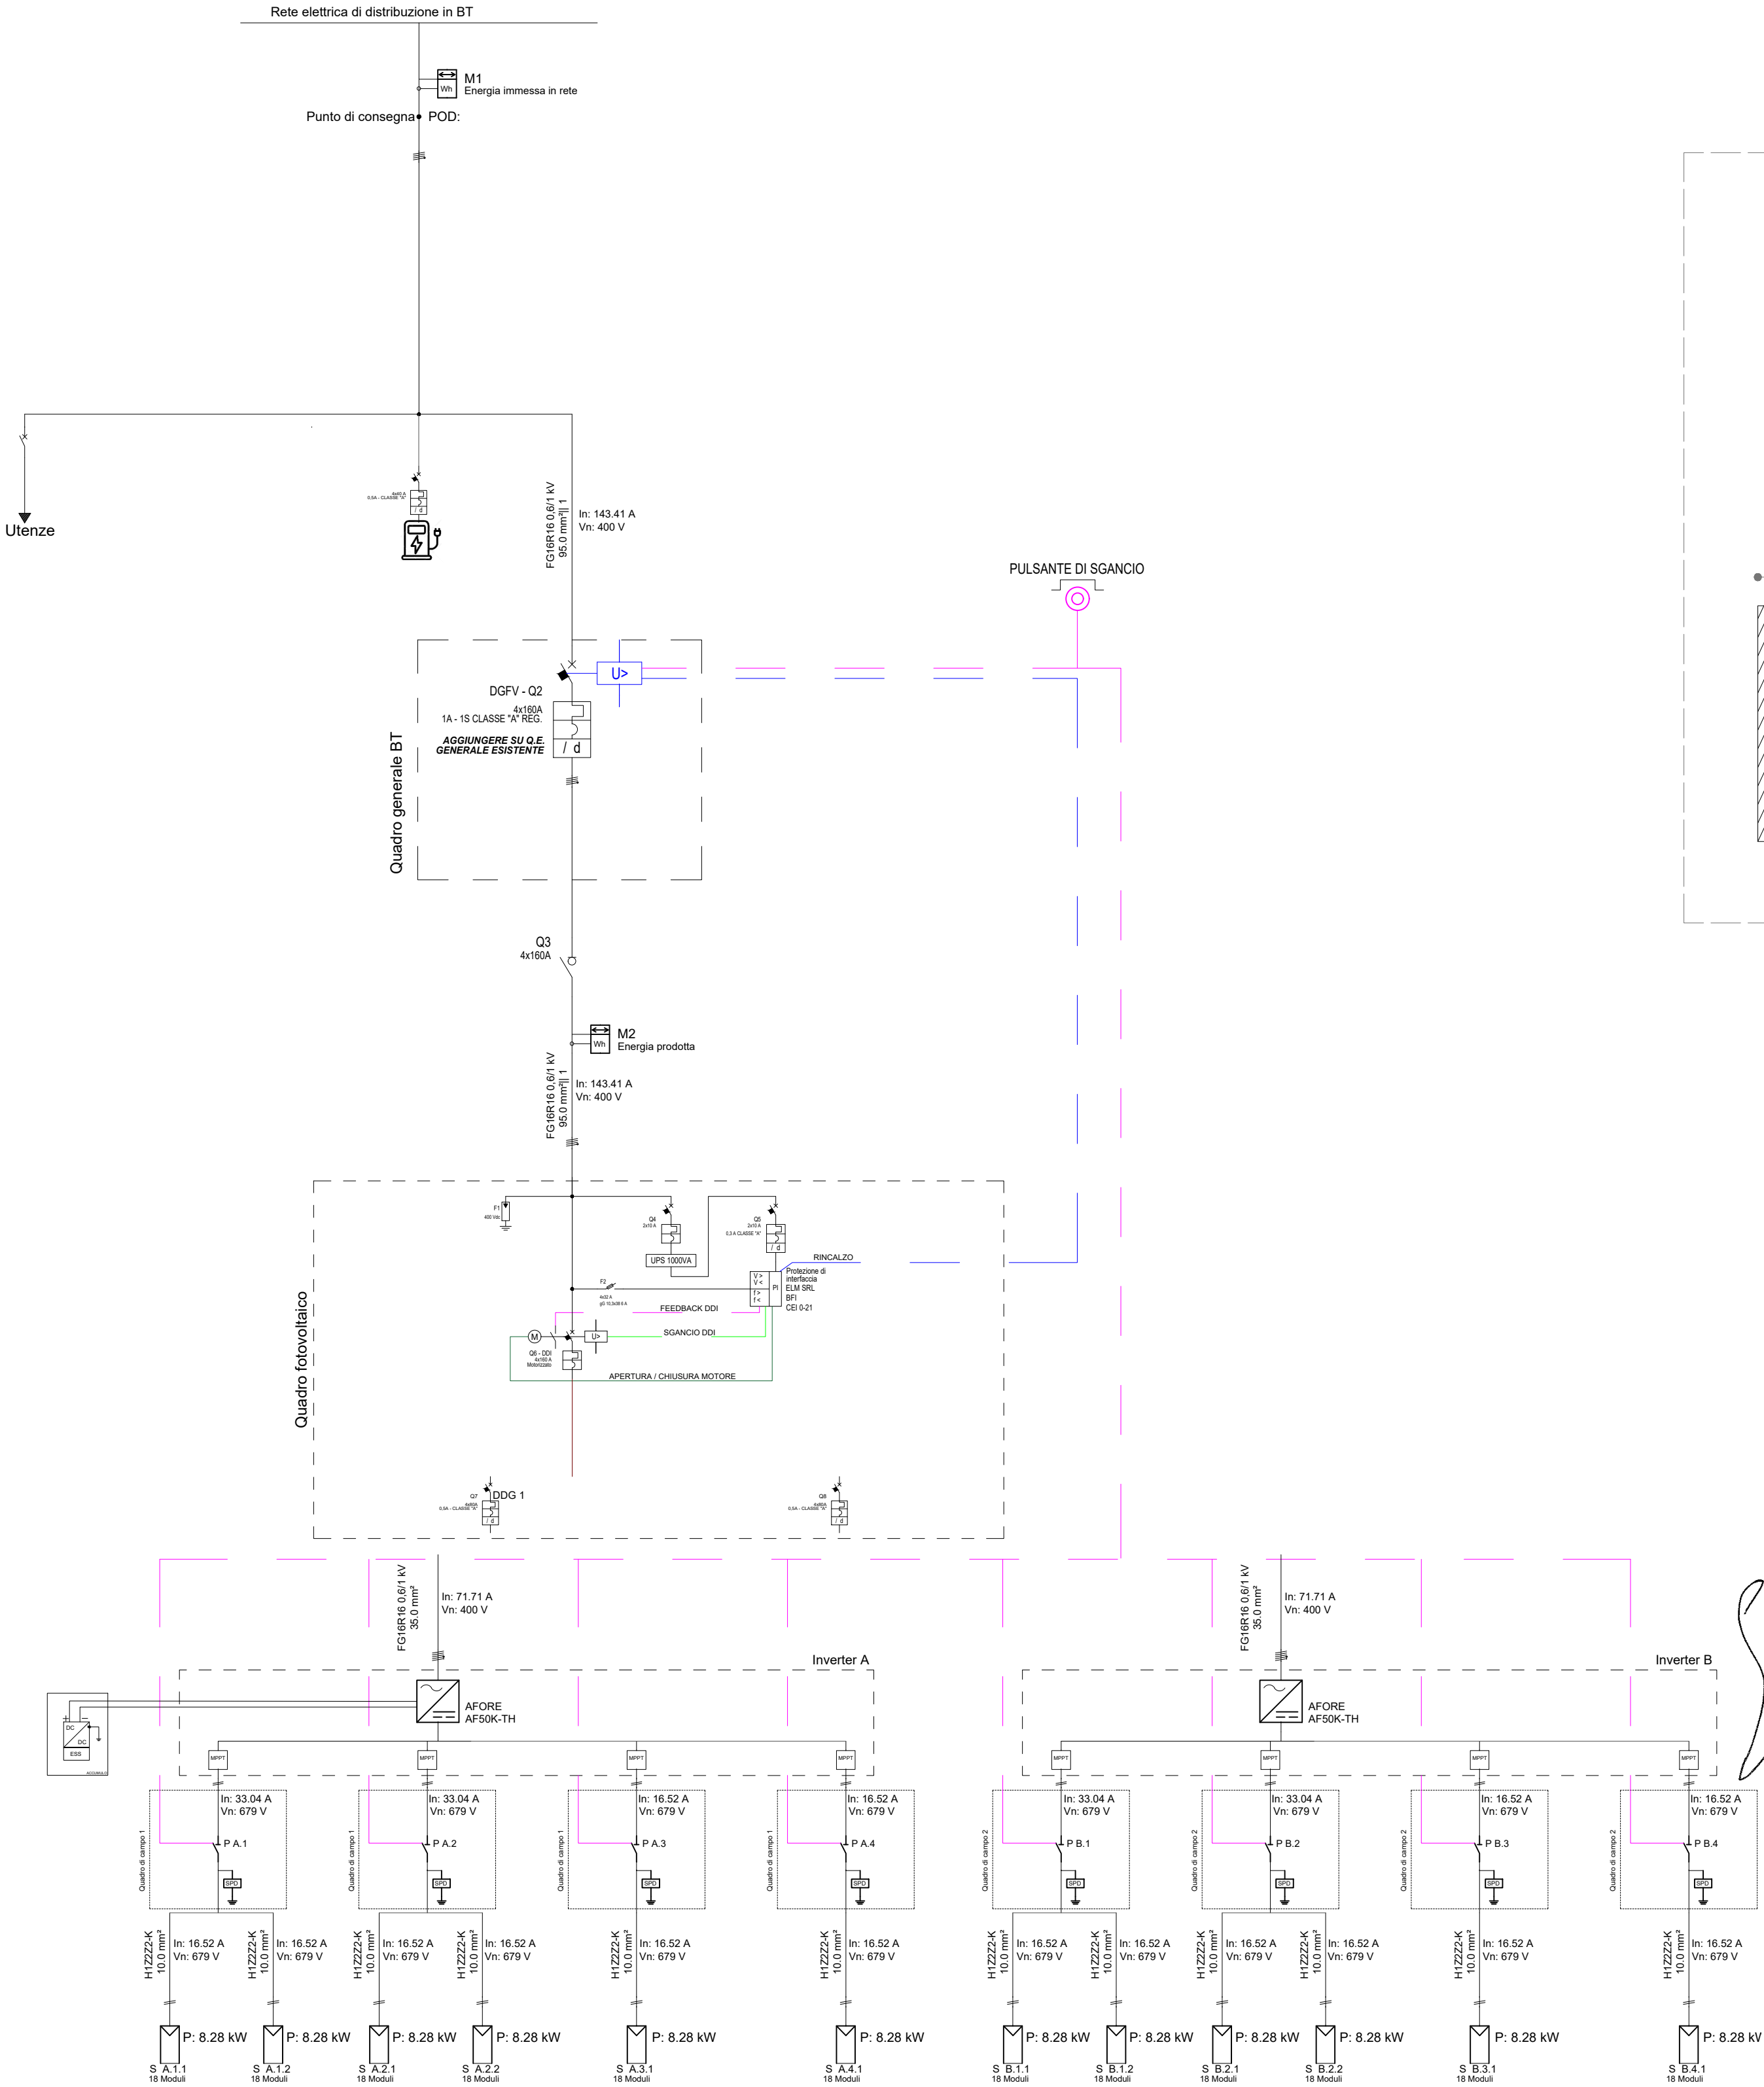


INVERTER

- (A-B)50 kW
Marca: AFORE
Modello: AF50K-TH

ACCUMULO

- 51,2 kWh
Marca: Dongguan Lithium Valley Energy Co., Ltd.
Modello: HS5-5A

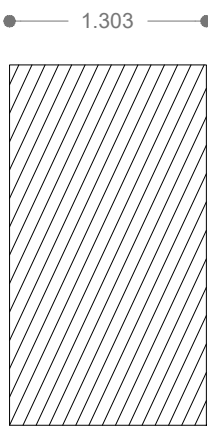

MODULO FOTOVOLTAICO
MARCA: 3SUN
TIPO: 3SHBGA-AF-460
POTENZA: 460 W
n. 216 MODULI
POTENZA NOMINALE 99,36kWp


DETTAGLIO IMPIANTO FOTOVOLTAICO
Inverter - Accumulo e Moduli utilizzati

FELETTO ING. GIORGIO
Viale Istria 50 - Conegliano (TV)

SCHEMA UNIFILARE
IMPIANTO FOTOVOLTAICO

99,36 KW

Guglielmi stalla

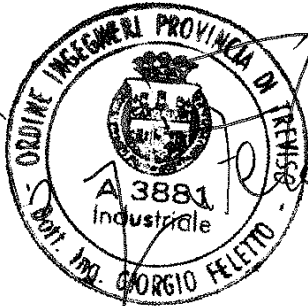

COMMITENTE:
Guglielmi Claudio srl
Via Cavallara 19, Valdastico (VI)

PROGETTO:
SCHEMA UNIFILARE IMPIANTO FOTOVOLTAICO DA 99,36 KW
Guglielmi Claudio -

REV. N.	DATA	FASE	
00	30/03/2026		

TAV.
02